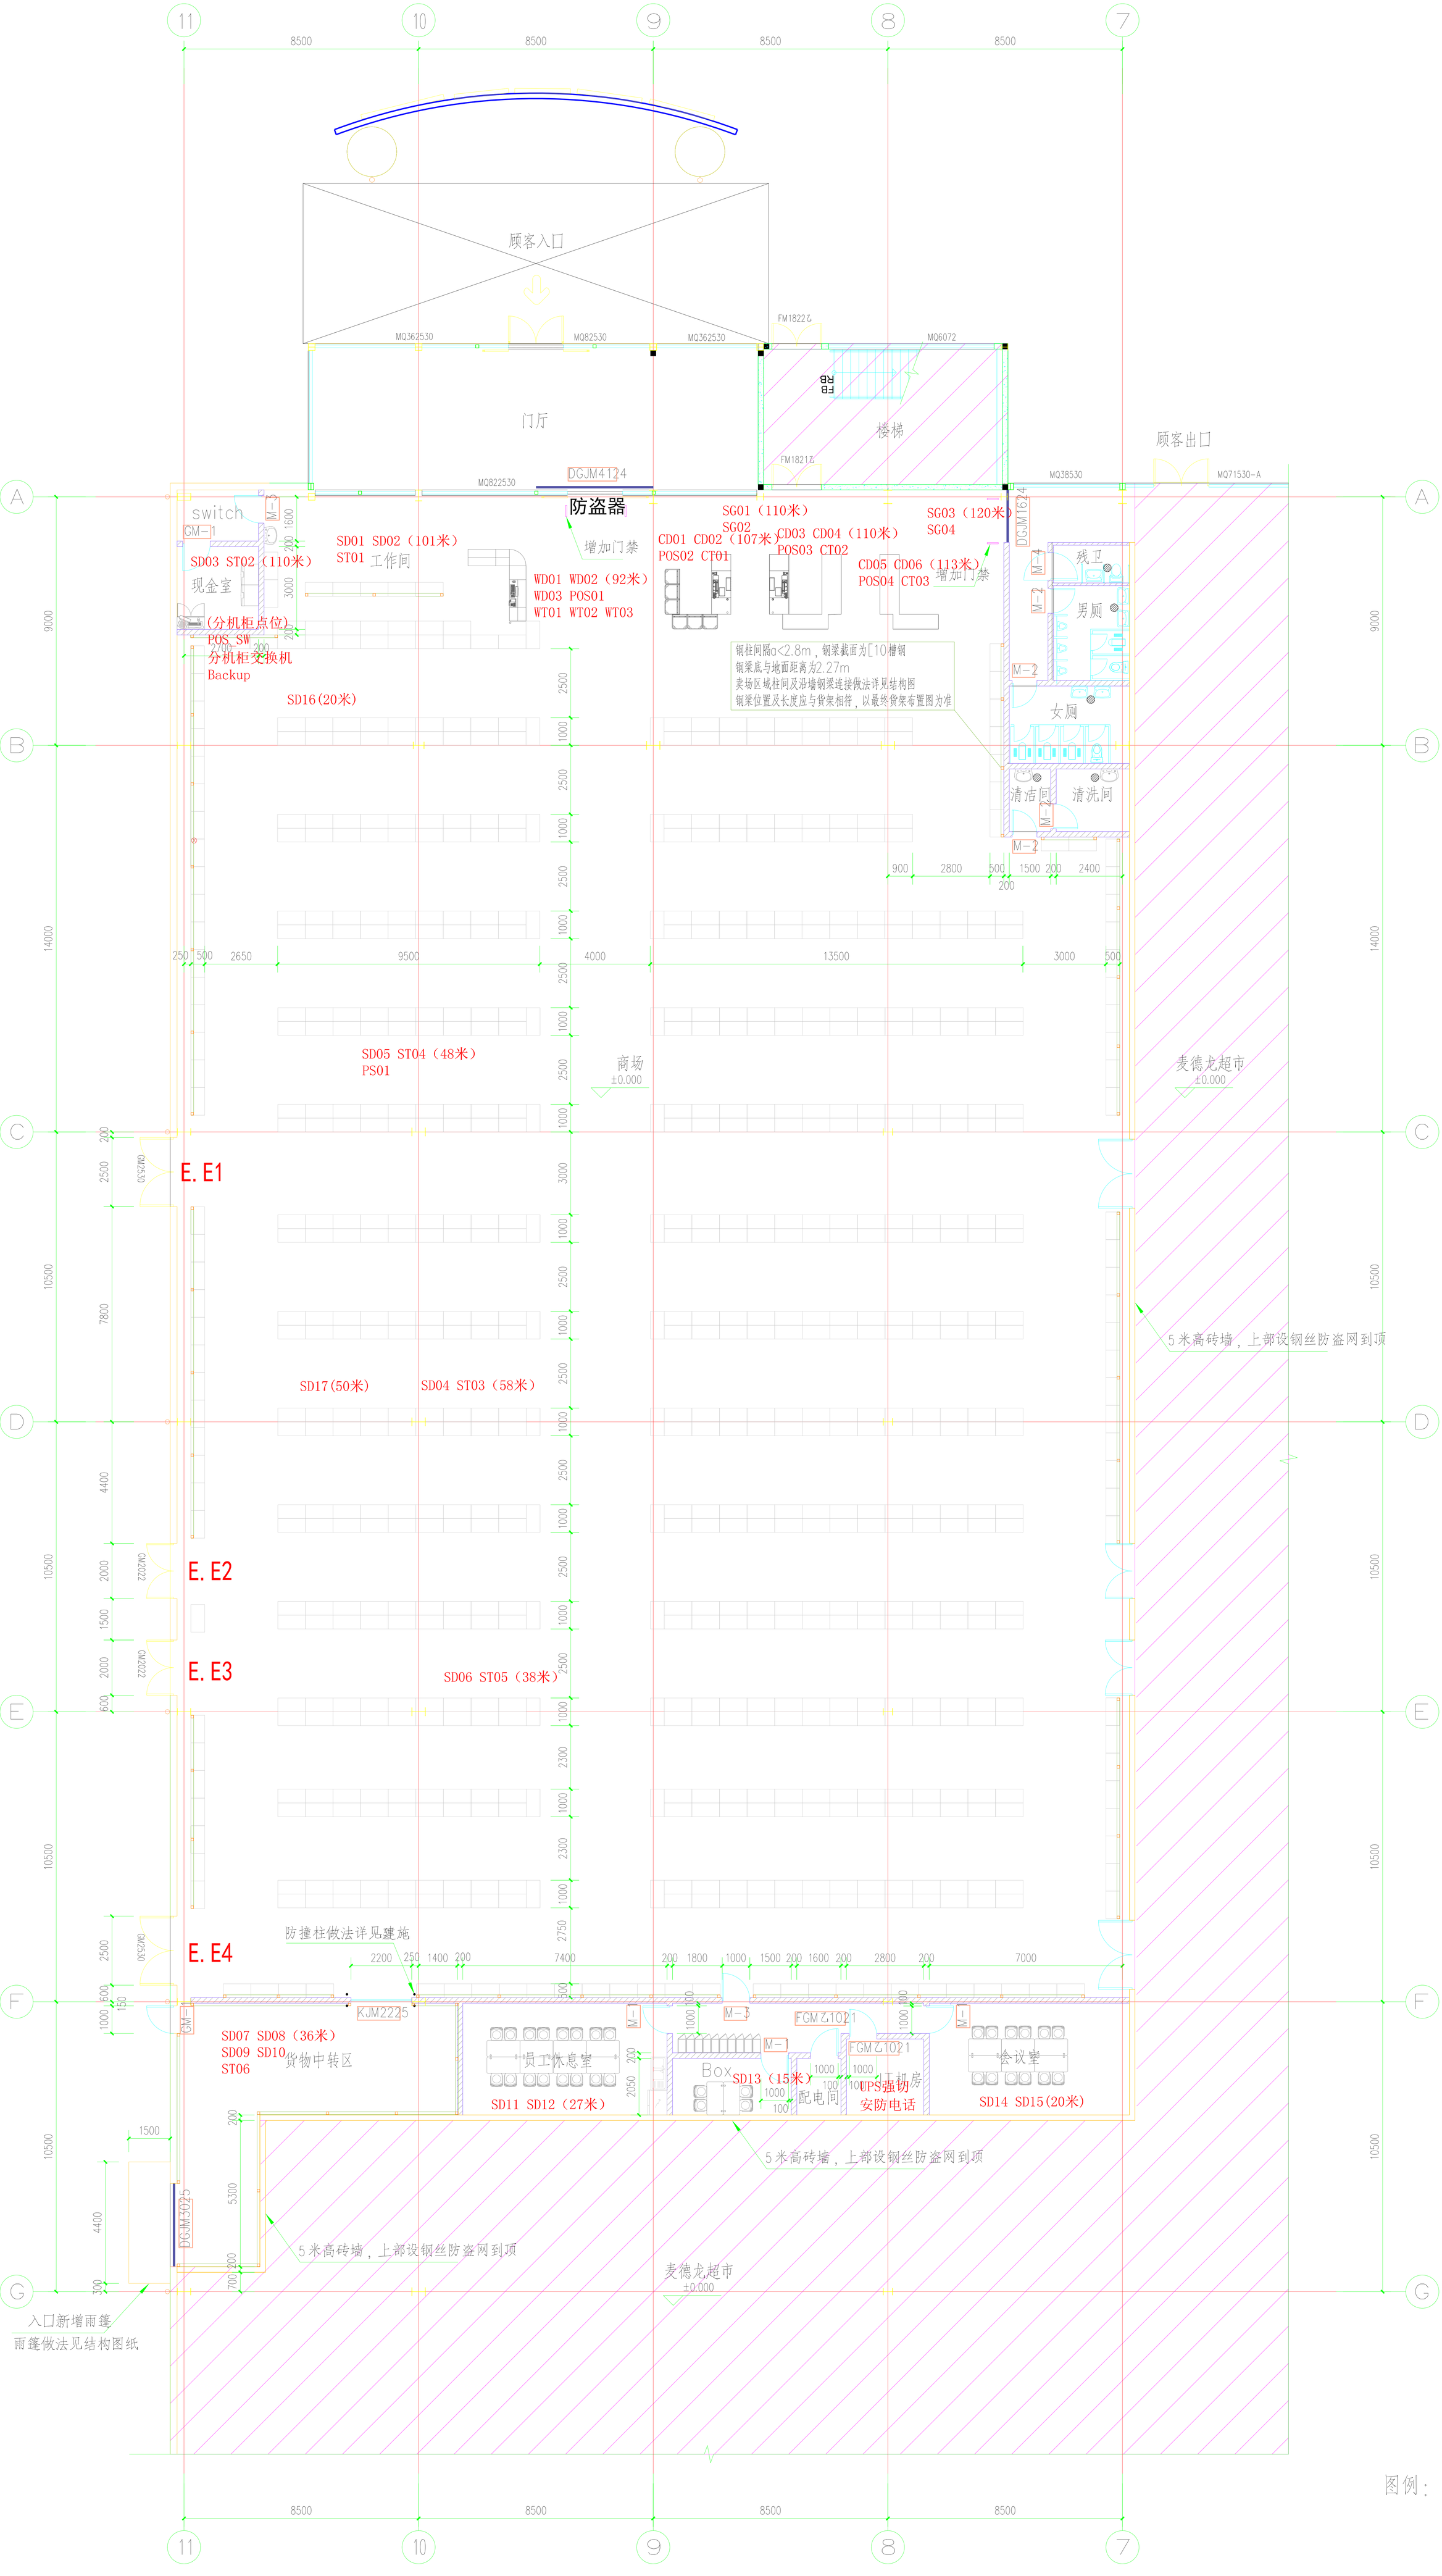

一层土建修改平面图 1:150

图例：

非本次设计范围

M—1

本次设计新增的门窗编号